
SUPPLY NETWORK WITH VAV INLETS

Actual saved horizontal material section at assumed z=0 | scale1:200

129 bodies;20outlets;full pressure unresolved (32fitting paths)

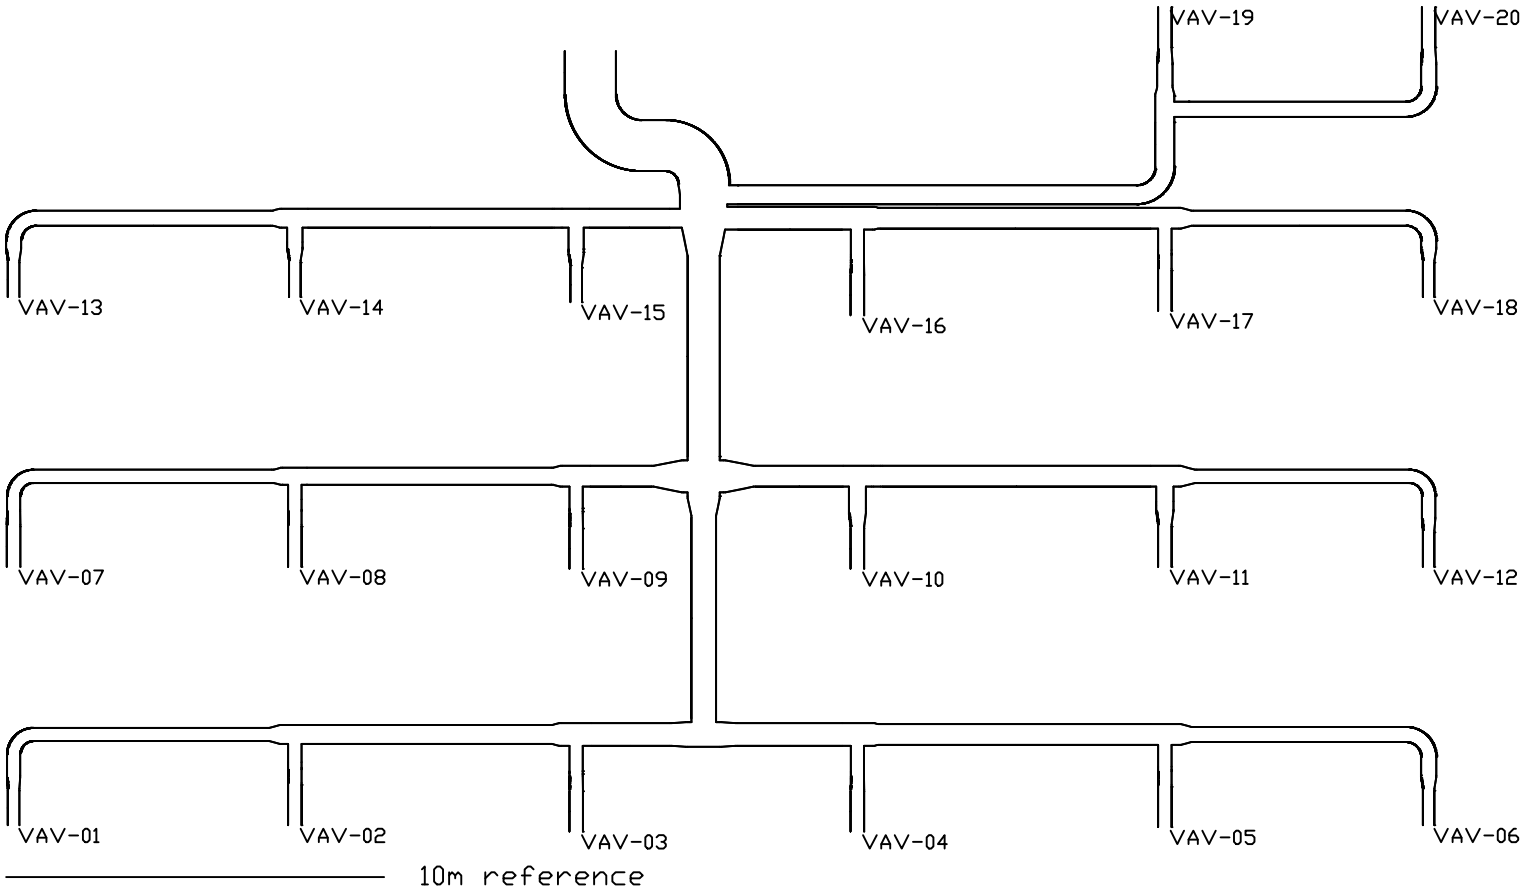

Nominal profiles, gauge and equipment inlet positions remain study assumptions

VAV internals, outlet plenums, flex, architecture and installed clearance remain unverified