
SUPPLY AND 3D BRANCH CONNECTION CANDIDATE

Saved main material section + actual branch-axis plan projection | 1:200

164main bodies +320branch pieces;80terminal turns;equipment internal flow unconnected

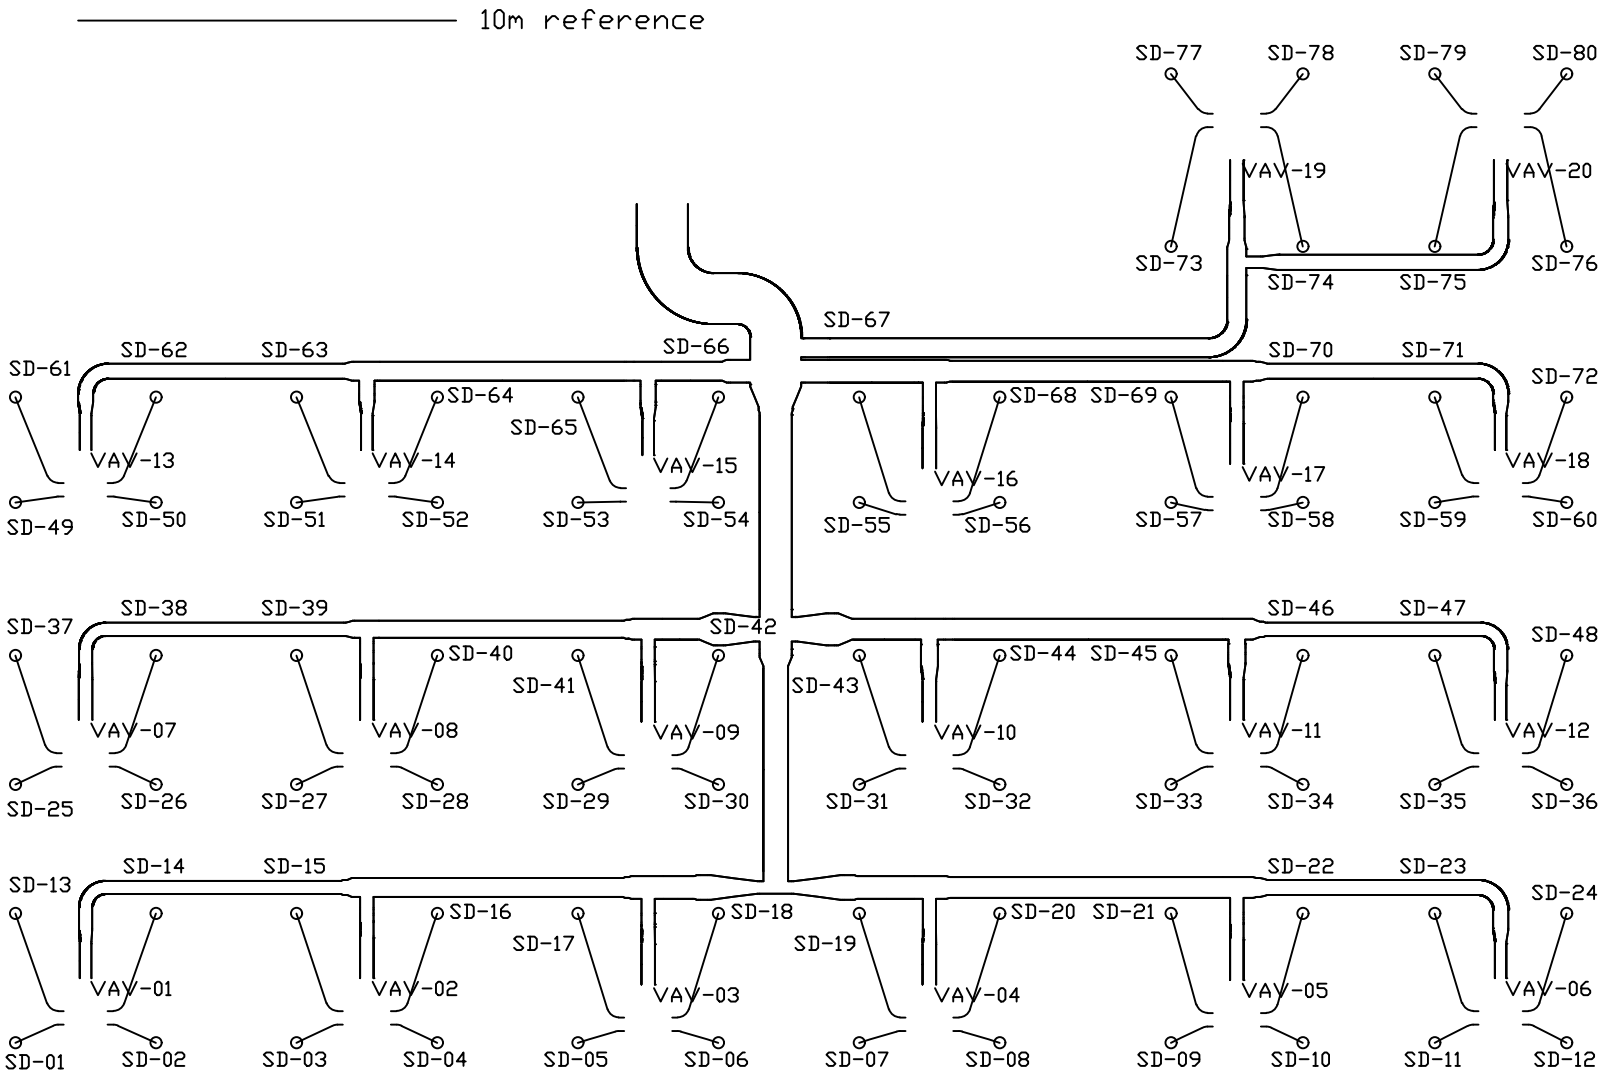

Branch proxy: nominal8in,R=1.5D,304.8mm drop ASSUMED;actual ceiling/neck height unknown

Main114conditional/4gaps only;branch product,bend losses,installation and full pressure unresolved